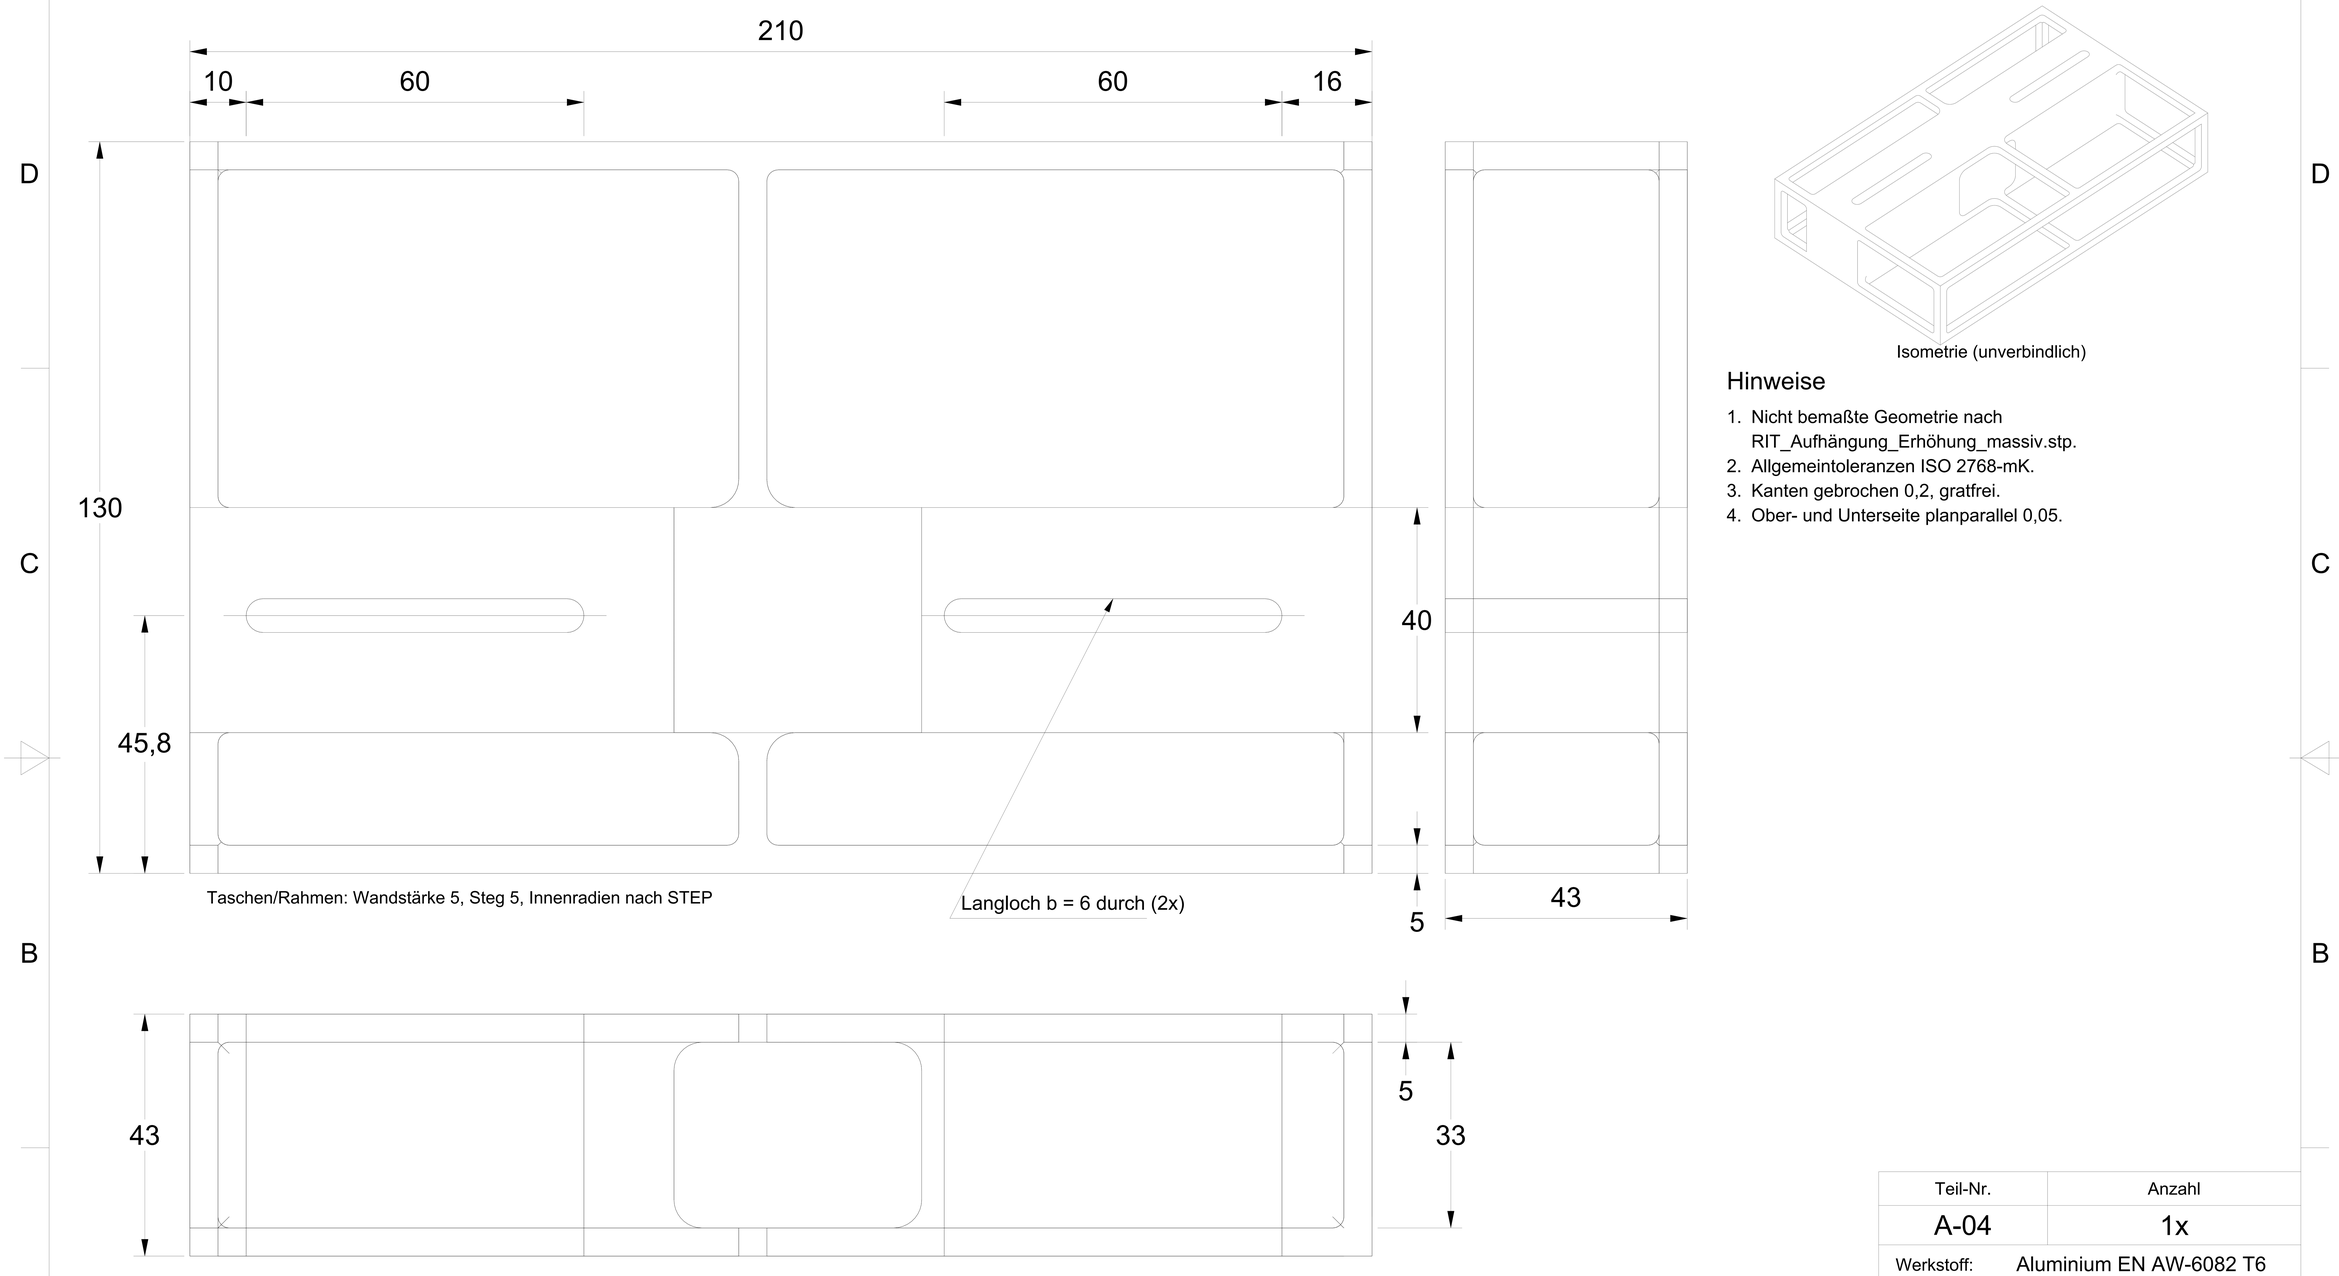

Isometrie (unverbindlich)

Hinweise

1. Nicht bemaßte Geometrie nach RIT_Aufhängung_Erhöhung_massiv.stp.
2. Allgemeintoleranzen ISO 2768-mK.
3. Kanten gebrochen 0,2, gratfrei.
4. Ober- und Unterseite planparallel 0,05.

Teil-Nr.	Anzahl
A-04	1x
Werkstoff:	Aluminium EN AW-6082 T6

Fachbereich 07

2026	Datum	Name
Entw.	26.10.	Wehkamp
Gez.	26.10.	Wehkamp
Gepr.	00.00.	name

Erhöhung RIT-Halter

Ansprechpartner
Konrad Wehkamp (konrad.helmut.wehkamp@physik.uni-giessen.de)
Jana Zorn(jana.zorn-2@exp1.physik.uni-giessen.de)

RIT_Aufhängung_Erhöhung_massiv.stp

Blatt 1/1

*H=HELICOIL, *E=ENSAT, *EB=ENTLÜFTUNGSBOHRUNG, *AG=ABGESTIMMT MIT GEGENSTÜCK, *DF=DICHTFLÄCHE KEINE KRATZER